




A. Planta general esquemática de una terminal (misma disposición en los dos portales)

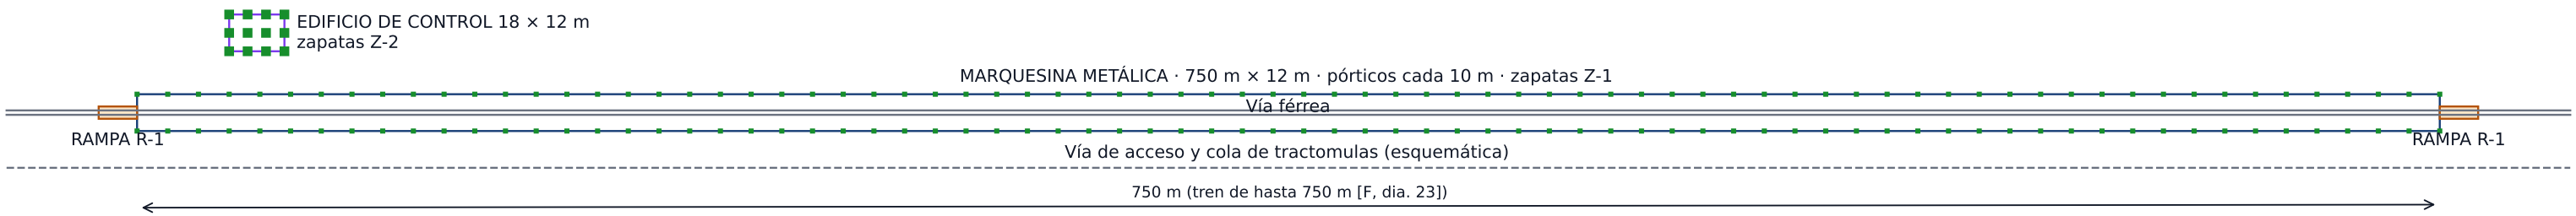


A'. Detalle del extremo de la terminal (rampa, primeros pórticos y edificio)

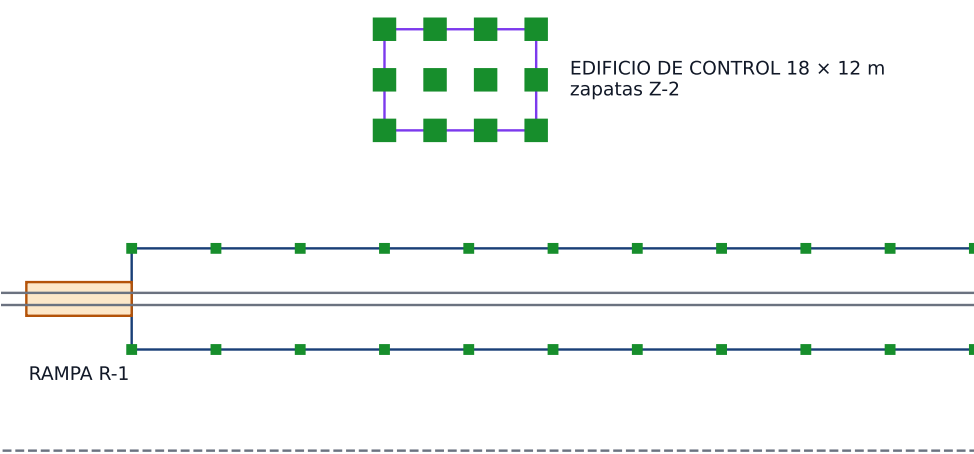

B. Zapata Z-1 (marquesina)

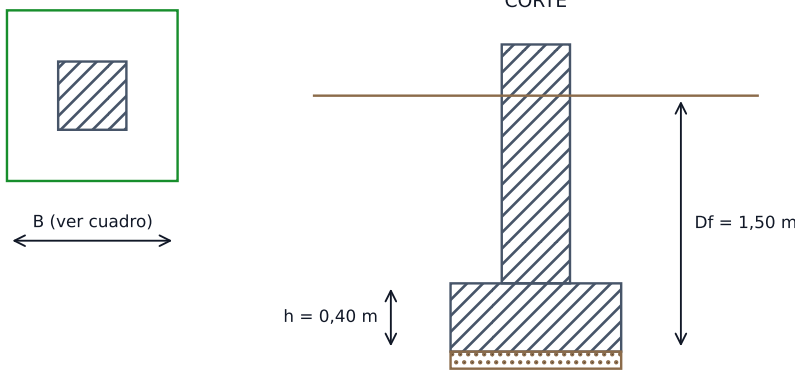

C. Zapata Z-2 (edificio de control)

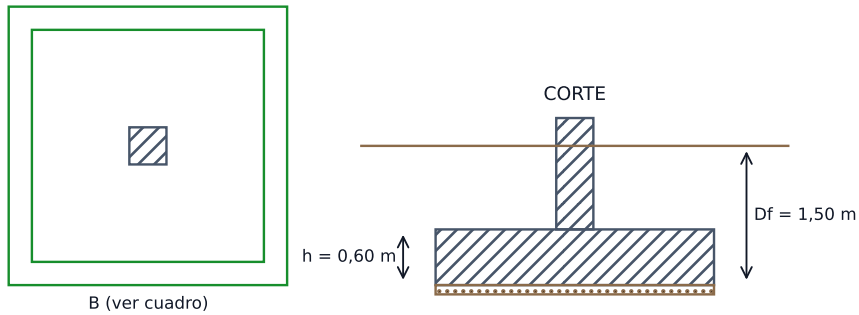

D. Corte longitudinal de la rampa R-1



E. Cuadro de cimentaciones (caso típico, NF en la base)

Elemento	Estructura	P servicio (kN)	B oriental S1 (m)	B occidental S2 (m)	h (m)
Z-1	Marquesina metálica del andén de carga	53	1,0	1,0	0,40
Z-2	Edificio de control, 2 pisos, pórticos de concreto	701	2,5	3,0	0,60
R-1	Rampa de tractomulas (3S3)	42 kPa	losa sobre terreno	losa sobre terreno	0,25

- ESQUEMA CONCEPTUAL, NO APTO PARA CONSTRUCCIÓN. Parámetros del suelo análogos (Act 3) y admisible como rango (Act 4).
- B adoptado = caso típico con NF en la base; zapatas cuadradas, carga centrada; Df y p_{adm} = 25 mm de la Act 4.
- Con los parámetros MÍNIMOS ninguna zapata aislada ≤ 6 m sirve para el edificio y la rampa exige sustituir el suelo: la exploración (NSR-10 H.3) decide.
- No incluye viento (NSR-10 B.6), que puede gobernar el arranque de la marquesina, ni el diseño estructural (NSR-10 C.15).